


Punkte	
◦	Adresspoint
△	Duct_Join
•	Duct_Ende
○	POP
●	Dp
□	Manhole
Linie	
---	Dropduct [200]
Duct	
—	Black
—	Blue
—	Green
—	Orange
—	Purple
Polygon	
□	DP_Cluster
□	POP_Cluster
DATA	
—	Backbone
□	Flurstück

Projekt	Hochhausen
Datum	11.03.2025
Maßstab	1:500
Blatt	HOCH_01 12/2
Bearbeiter	SEFA COSKUN

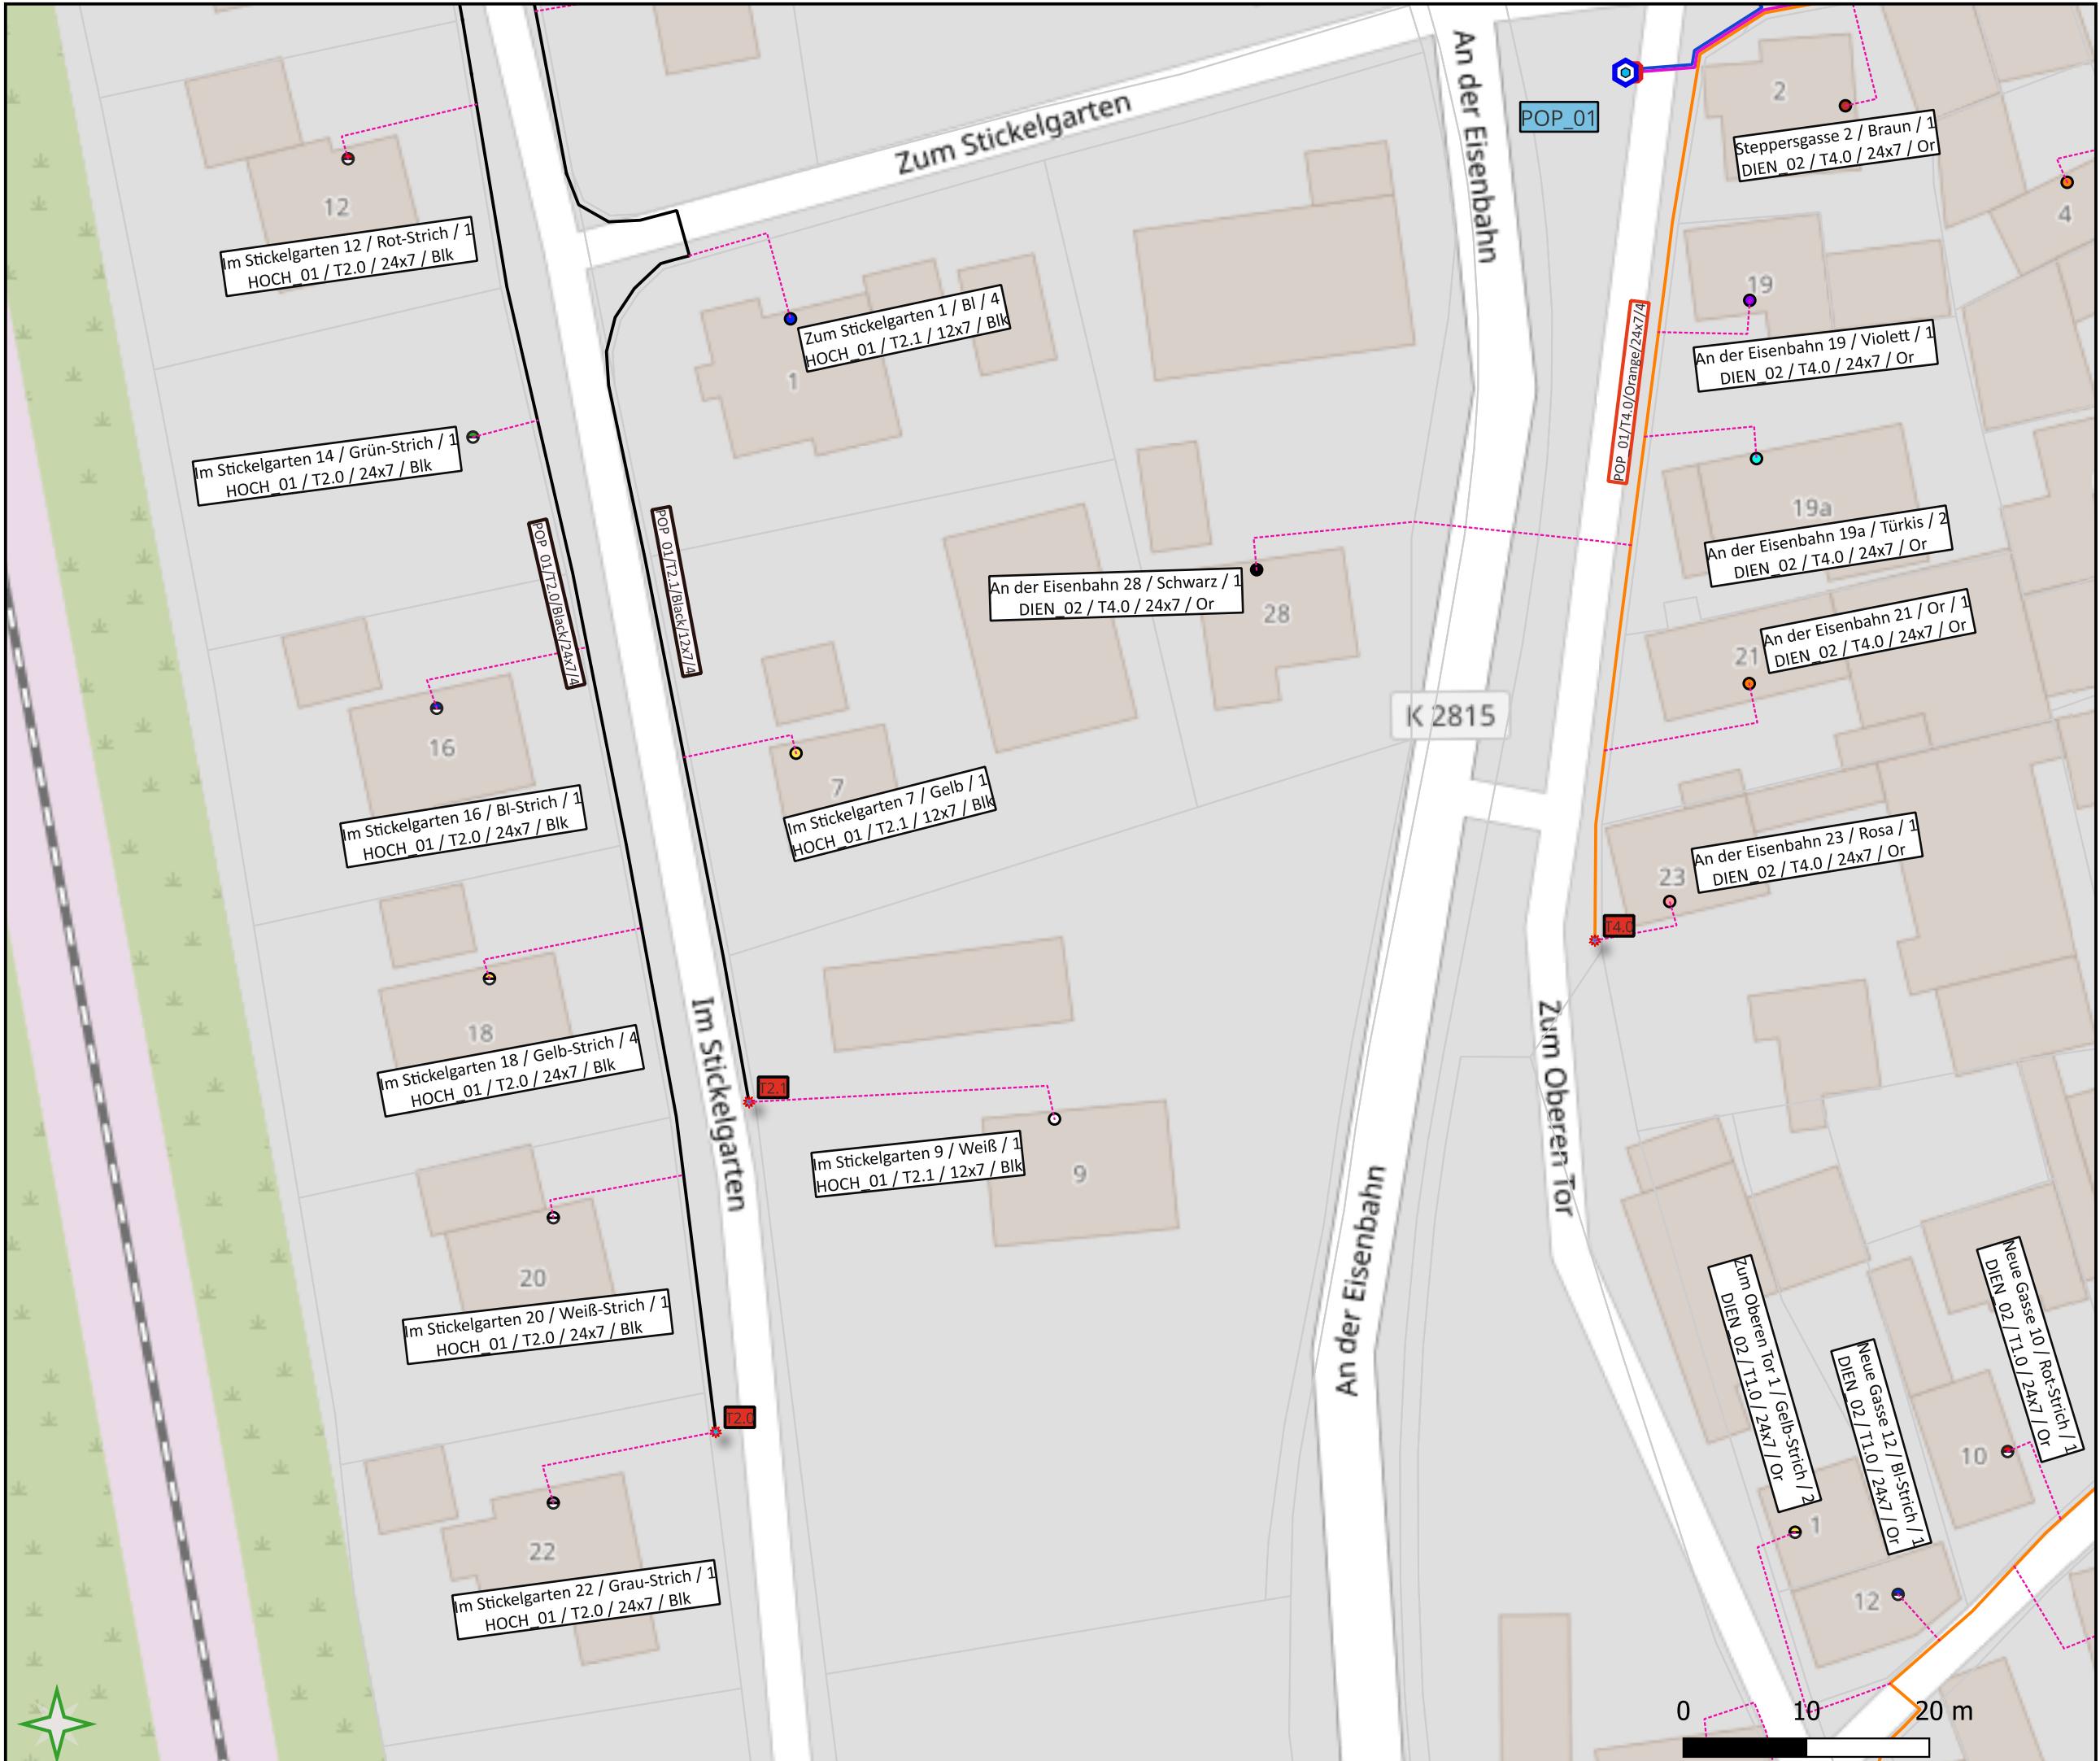



Punkte

- Adresspoint
 - ▲ Duct_Join
 - * Duct_Ende
 - Hexagon POP
 - Target Dp
 - Manhole

Linie

- Dropduct [200]

Duct

- Black
 - Blau
 - Green
 - Orange
 - Purple

Poligon


- DP_Cluster
 - POP Cluster

DATA

- Backbone
 - Flurstück

Projekt	Hochhausen
Datum	11.03.2025
Maßstab	1:500
Blatt	HOCH_01 12/3
Bearbeiter	SEFA COSKUN



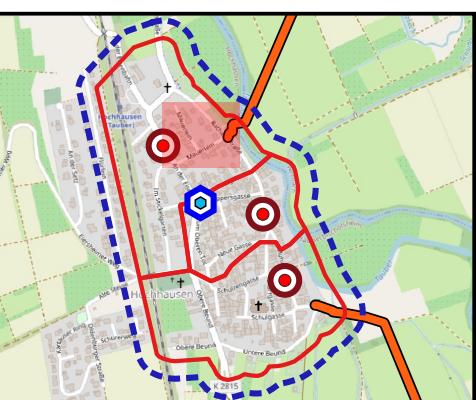

Punkte	
◦	Adresspoint
△	Duct_Join
*	Duct_Ende
○	POP
●	Dp
□	Manhole
Linie	
- - -	Dropduct [200]
Duct	
—	Black
—	Blau
—	Green
—	Orange
—	Purple
Poligon	
—	DP_Cluster
—	POP_Cluster
DATA	
—	Backbone
—	Flurstück

Projekt	Hochhausen
Datum	11.03.2025
Maßstab	1:500
Blatt	HOCH_02 12/4
Bearbeiter	SEFA COSKUN





Punkte

- Adresspoint
 - △ Duct_Join
 - * Duct_Ende
 - hexagon POP
 - circle Dp
 - square Manhole

Linie

- Dropuct [200]

Duct

- Black
 - Blau
 - Green
 - Orange
 - Purple

Poligon



-  DP_Cluster
 POP_Cluster

DATA


-  Backbone
 -  Flurstück



Projekt	Hochhausen
Datum	11.03.2025
Maßstab	1:500
Blatt	HOCH_01 12/5
Bearbeiter	SEFA COSKUN



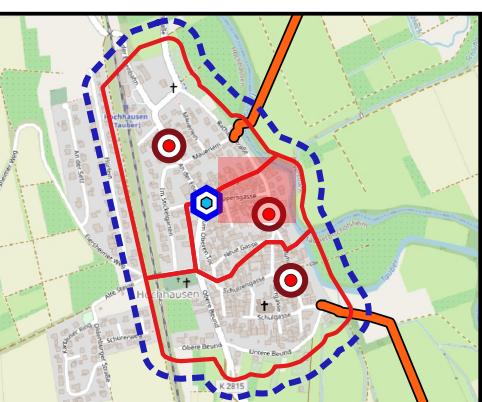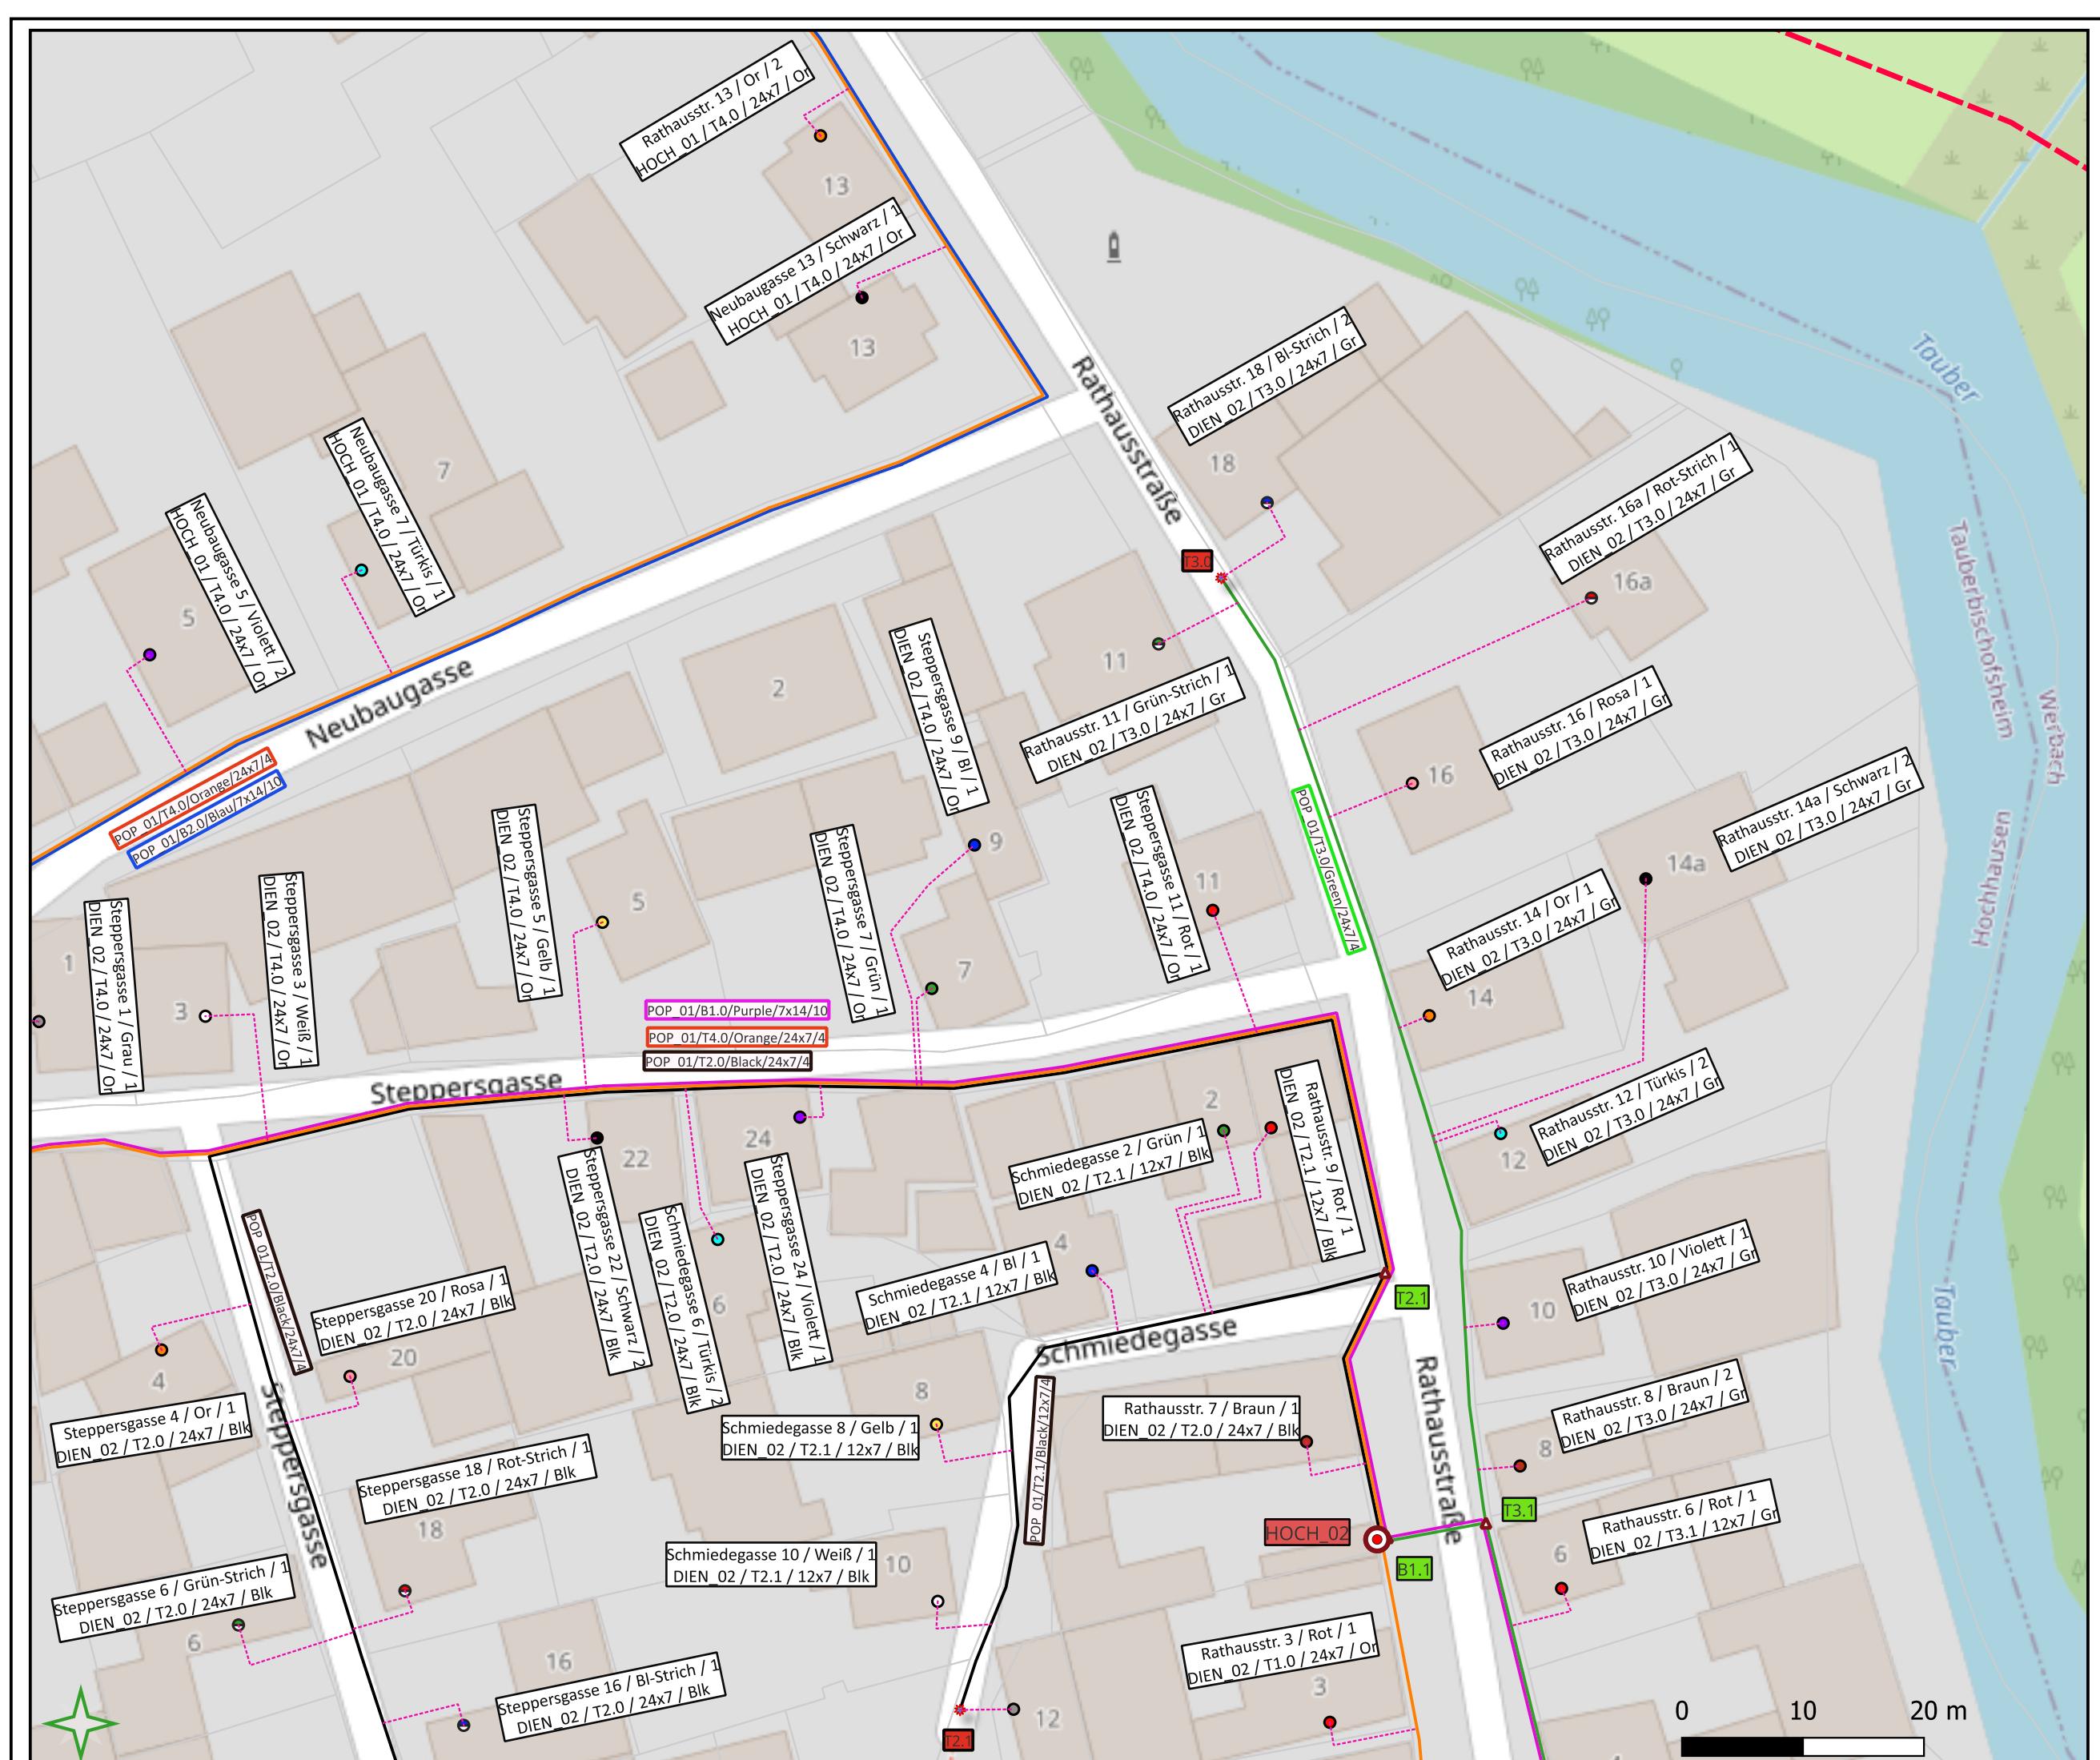

Projekt	Hochhausen
Datum	11.03.2025
Maßstab	1:500
Blatt	HOCH_02 12/6
Bearbeiter	SEFA COSKUN

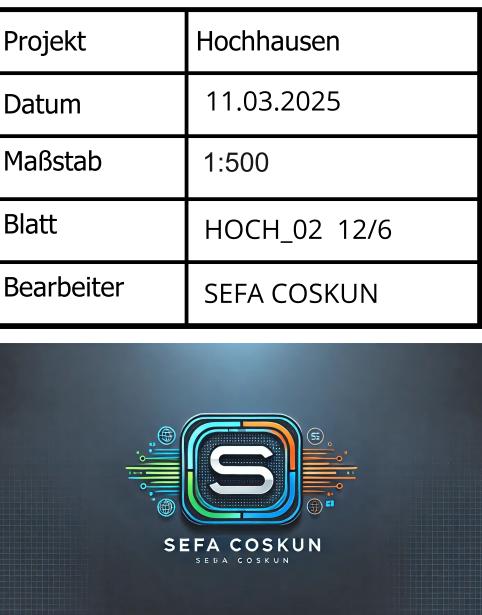


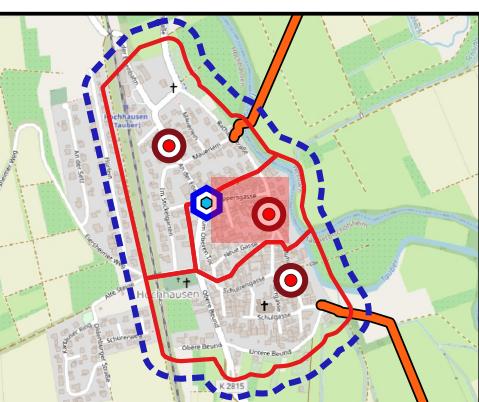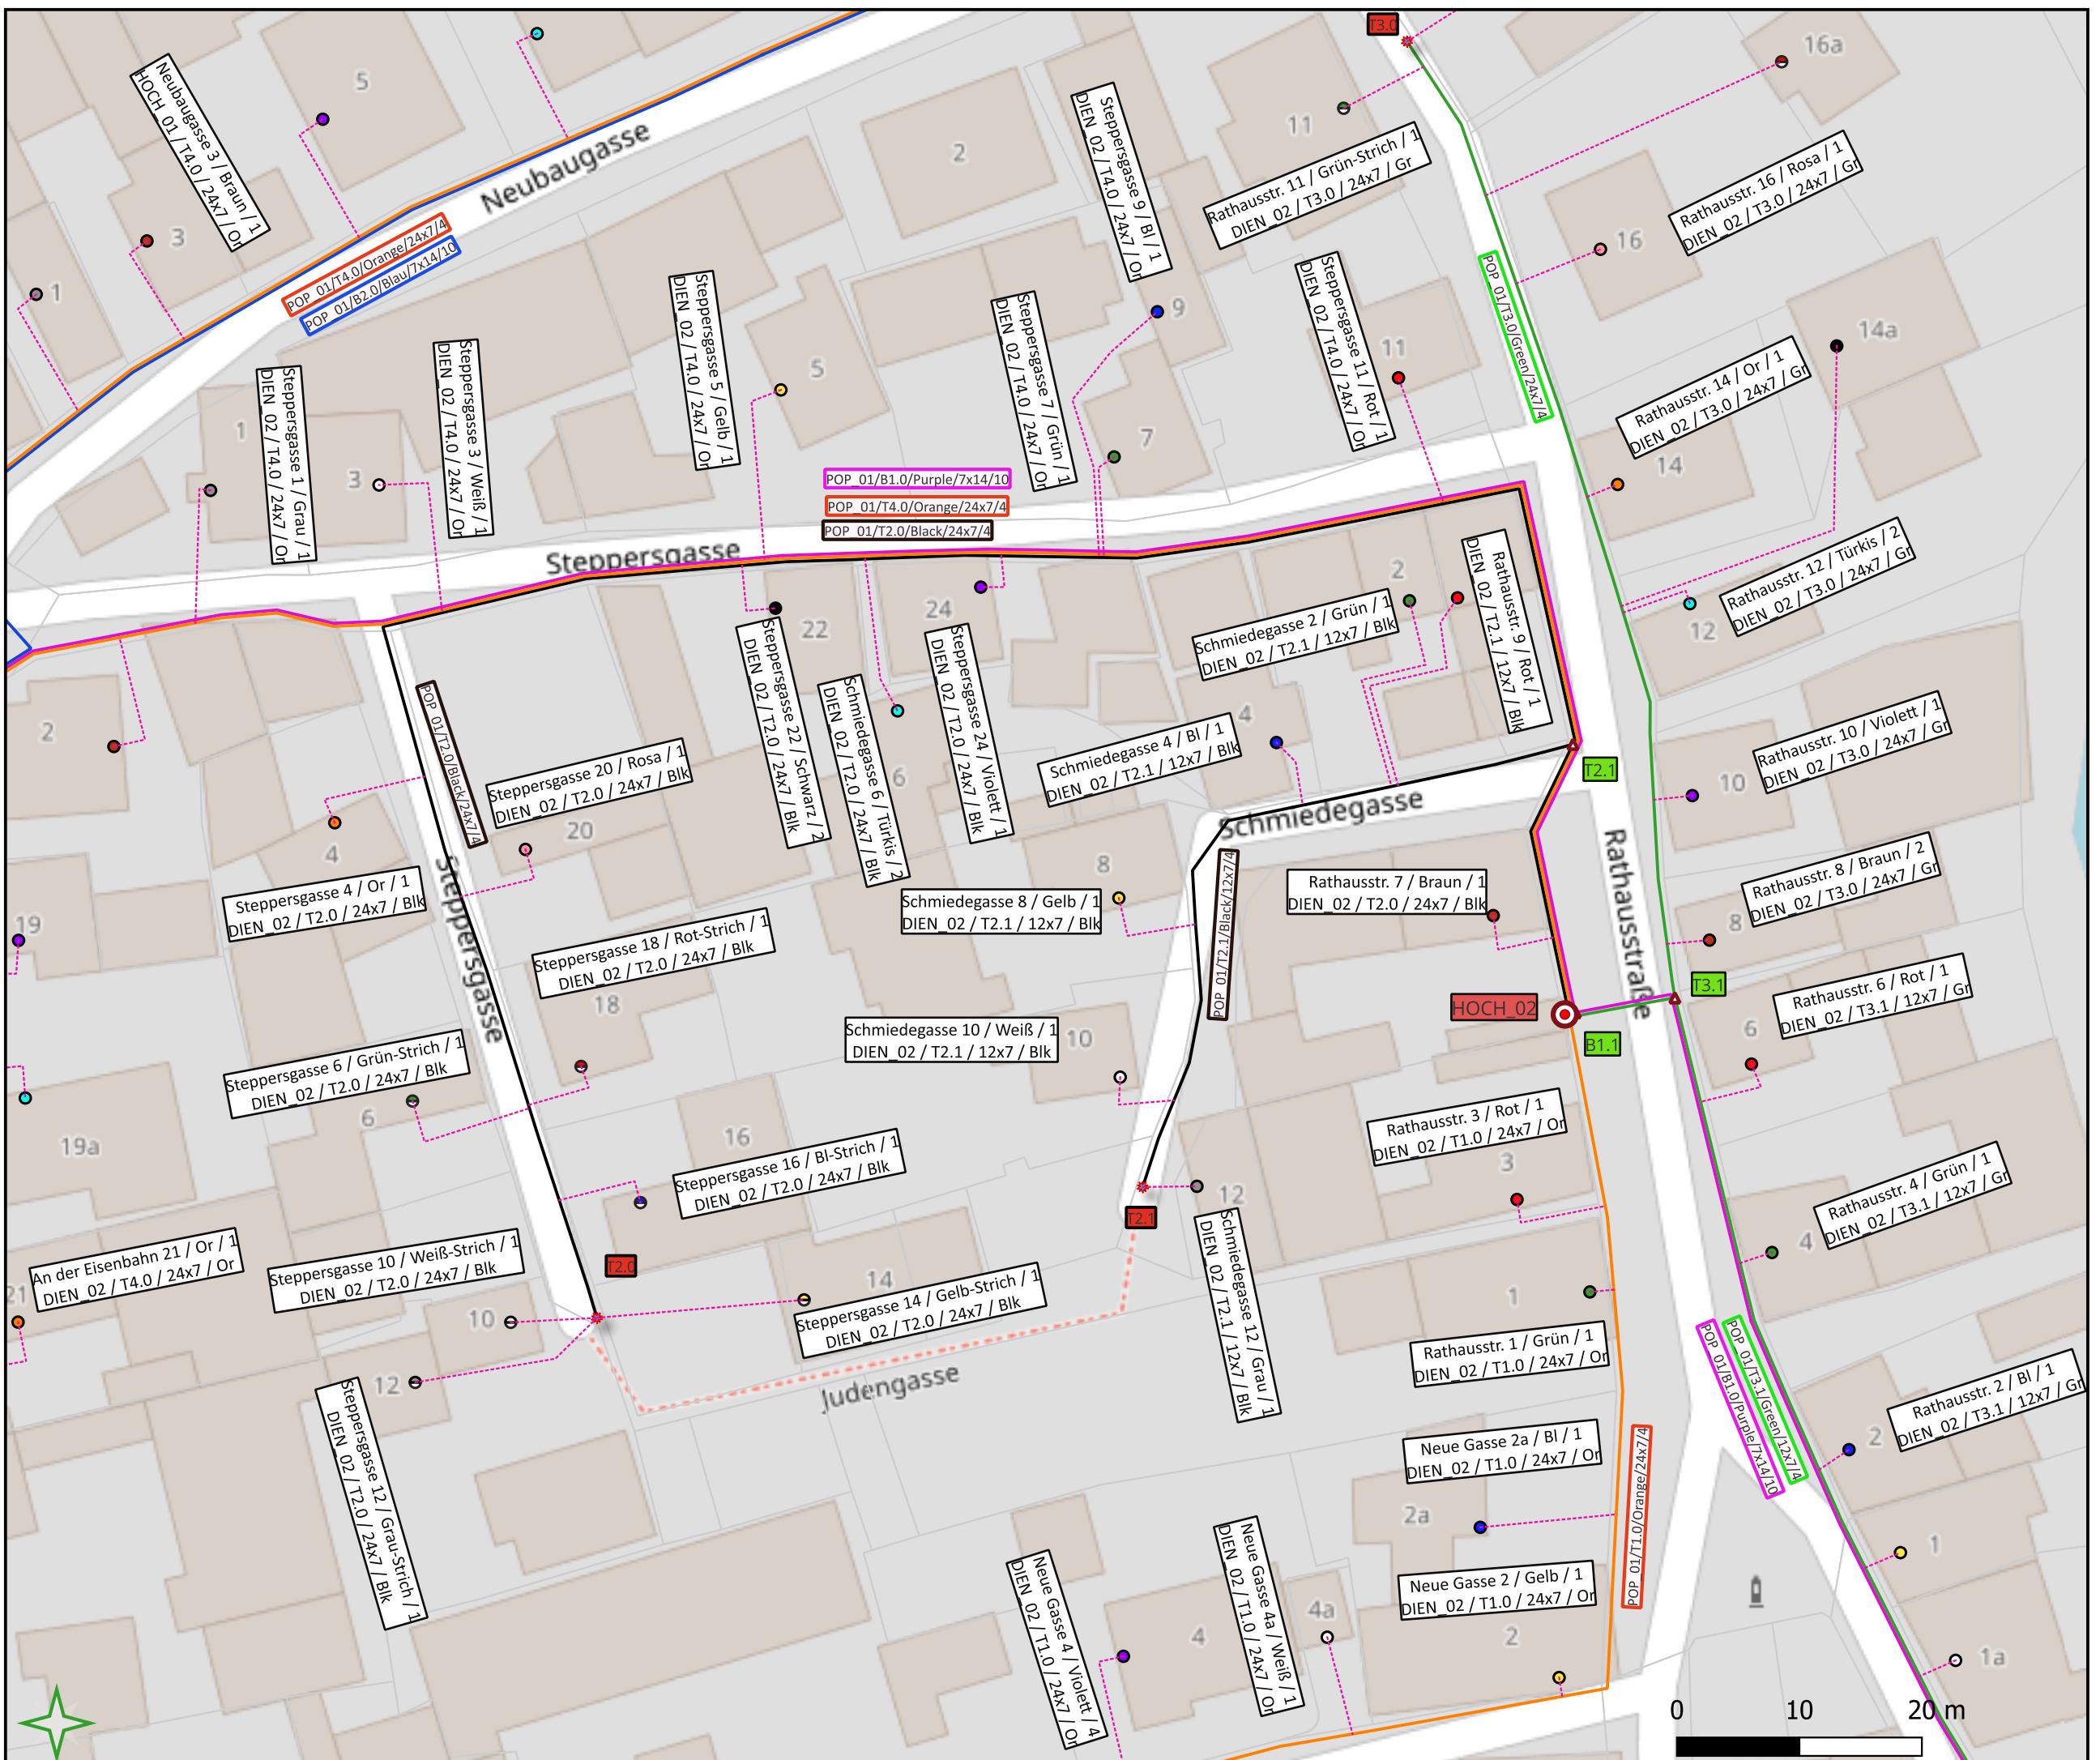

Punkte	
◦	Adresspoint
△	Duct_Join
*	Duct_Ende
○	POP
●	Dp
□	Manhole
Linie	
- - -	Dropduct [200]
Duct	
—	Black
—	Blau
—	Green
—	Orange
—	Purple
Poligon	
□	DP_Cluster
□	POP_Cluster
DATA	
—	Backbone
□	Flurstück

Projekt	Hochhausen
Datum	11.03.2025
Maßstab	1:500
Blatt	HOCH_02 12/7
Bearbeiter	SEFA COSKUN



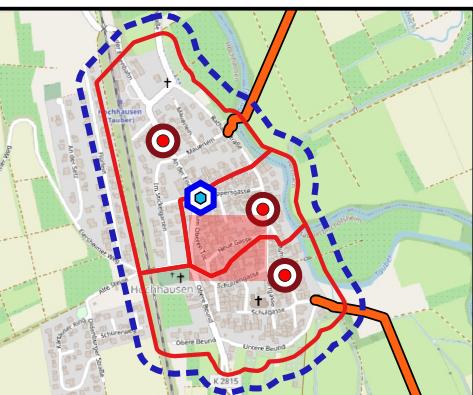

Punkte

- Adresspoint
- Duct_Join
- Duct_Ende
- POP
- Dp
- Manhole

Linie

- Dropduct [200]

Duct

- Black
- Blau
- Green
- Orange
- Purple

Poligon


- DP_Cluster
- POP_Cluster

DATA

- Backbone
- Flurstück


Projekt	Hochhausen
Datum	11.03.2025
Maßstab	1:500
Blatt	HOCH_02 12/8
Bearbeiter	SEFA COSKUN



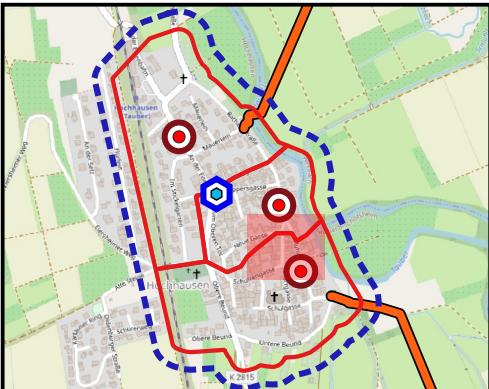


Projekt	Hochhausen
Datum	11.03.2025
Maßstab	1:500
Blatt	HOCH_03 12/9
Bearbeiter	SEFA COSKUN




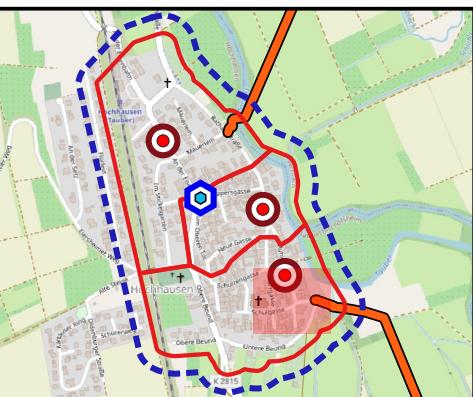

Projekt	Hochhausen
Datum	11.03.2025
Maßstab	1:500
Blatt	HOCH_03 12/10
Bearbeiter	SEFA COSKUN

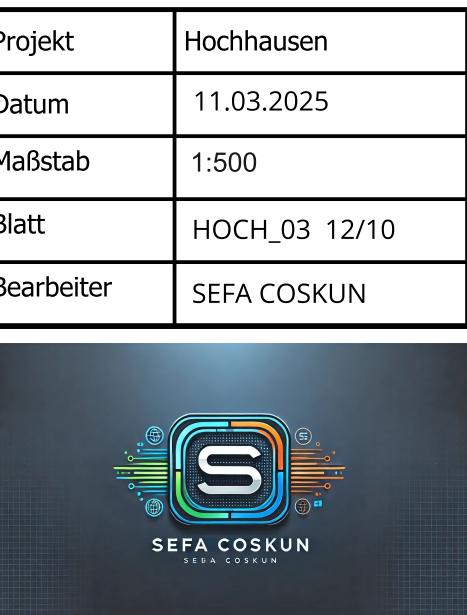



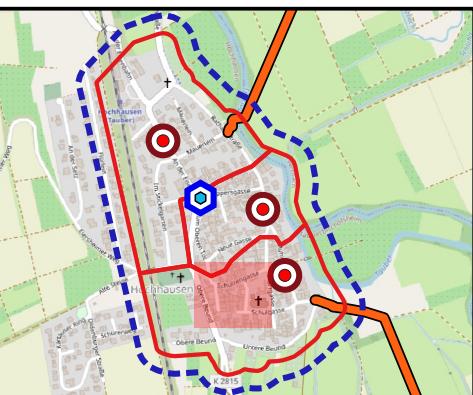

Projekt	Hochhausen
Datum	11.03.2025
Maßstab	1:500
Blatt	HOCH_03 12/12
Bearbeiter	SEFA COSKUN

